

This document is exclusively property of Schneider Electric and shall not be used or copied without authorization

1	2	3	4	5	6	7	8	
A								A
B								
C								
D								D
E								E
F								F
1	2	3	4	5	6	7	8	

A	9/25/2023 FSR	9/25/2023 HK	9/25/2023 TNN	FOR APPROVAL	FA
Rev	Date Established	Date Checked	Date Approved	Modifications	Status

End User :



PT. ANTAM Tbk.

Project :

GI 150KV ANTAM POMALAA - SAS & CRP

Contractor :



PT. HIGH VOLT TECHNOLOGY

Manufacturer :



PT. SCHNEIDER INDONESIA
INFRASTRUCTURE BUSINESS

	Name	Date	Remarks	Drawing title : SUBSTATION AUTOMATION SYSTEM ARCHITECTURE DIAGRAM
Drawn	FSR	9/25/2023	FA	
Checked	HK	9/25/2023	FA	
Approved	TNN	9/25/2023	FA	

Customer Order Number :

200/HVT-SCHNEIDERINDONESIA/ PO/VIII/2023 R1 - dated: 2023-08-14

Customer Drawing Number :

Drawing title :

COVER SHEET

Drawing number :

E2010-96317-BD-01-SAD

Revision

A


Size A3	Archive number	Scale NTS	Sheet 001	Next Sheet 002
------------	----------------	--------------	--------------	-------------------

This document is exclusively property of Schneider Electric and shall not be used or copied without authorization

1		2		3		4		5		6		7		8	
A		LEGEND														A	
B		<table><tr><th colspan="2">EQUIPMENT</th><th colspan="2">DESCRIPTION</th><th colspan="2">EQUIPMENT</th><th colspan="2">DESCRIPTION</th><th colspan="4">LINK COLOR</th></tr><tr><td colspan="2"></td><td colspan="2">SERVER / WORKSTATION ADVANTECH</td><td colspan="2"></td><td colspan="2">ETHERNET SWITCH KYLAND</td><td colspan="2"></td><td colspan="4">FIBER OPTIC PATCH CORD MULTIMODE</td></tr><tr><td colspan="2"></td><td colspan="2">BAY CONTROL UNIT / COMMON IED IO SCHNEIDER ELECTRIC</td><td colspan="2"></td><td colspan="2">PROTECTION RELAY SCHNEIDER ELECTRIC MICOM</td><td colspan="2"></td><td colspan="4">UTP CAT-4 CABLE</td></tr><tr><td colspan="2"></td><td colspan="2">ETHERNET SWITCH KYLAND</td><td colspan="2"></td><td colspan="2"></td><td colspan="2"></td><td colspan="4">RS232/RS485 CABLE</td></tr><tr><td colspan="2"></td><td colspan="2">ROUTER</td><td colspan="2"></td><td colspan="2"></td><td colspan="2"></td><td colspan="4">COAXIAL CABLE</td></tr><tr><td colspan="2"></td><td colspan="2">PROTECTION RELAY SCHNEIDER ELECTRIC MICOM</td><td colspan="2"></td><td colspan="2"></td><td colspan="2"></td><td colspan="4">VGA, KEYBOARD, MOUSE CABLE</td></tr><tr><td colspan="2"></td><td colspan="2">AUTOMATIC VOLTAGE REGULATOR A-EBERLE (REG-DA)</td><td colspan="2"></td><td colspan="2"></td><td colspan="4"></td><td colspan="2"></td></tr><tr><td colspan="2"></td><td colspan="2">MODEM DCE (IG202T)</td><td colspan="2"></td><td colspan="2"></td><td colspan="4"></td><td colspan="2"></td></tr><tr><td colspan="2"></td><td colspan="2">GATEWAY SCHNEIDER ELECTRIC SAITEL DP</td><td colspan="2"></td><td colspan="2"></td><td colspan="4"></td><td colspan="2"></td></tr><tr><td colspan="2"></td><td colspan="2">ENERGY METER SCHNEIDER ELECTRIC (ION 8650)</td><td colspan="2"></td><td colspan="2"></td><td colspan="4"></td><td colspan="2"></td></tr><tr><td colspan="2"></td><td colspan="2">MONITOR</td><td colspan="2"></td><td colspan="2"></td><td colspan="4"></td><td colspan="2"></td></tr><tr><td colspan="2"></td><td colspan="2">KEYBOARD & MOUSE</td><td colspan="2"></td><td colspan="2"></td><td colspan="4"></td><td colspan="2"></td></tr><tr><td colspan="2"></td><td colspan="2">SPEAKER</td><td colspan="2"></td><td colspan="2"></td><td colspan="4"></td><td colspan="2"></td></tr><tr><td colspan="2"></td><td colspan="2">ANTENNE GPS</td><td colspan="2"></td><td colspan="2"></td><td colspan="4"></td><td colspan="2"></td></tr><tr><td colspan="2"></td><td colspan="2">GPS TIME REFERENCE CLOCK HOPF 8030HEPTA</td><td colspan="2"></td><td colspan="2"></td><td colspan="4"></td><td colspan="2"></td></tr><tr><td colspan="2"></td><td colspan="2">LASER PRINTER</td><td colspan="2"></td><td colspan="2"></td><td colspan="4"></td><td colspan="2"></td></tr><tr><td colspan="2"></td><td colspan="2">ENGINEERING WORKSTATION</td><td colspan="2"></td><td colspan="2"></td><td colspan="4"></td><td colspan="2"></td></tr><tr><td colspan="2"></td><td colspan="2">KVM EXTENDER</td><td colspan="2"></td><td colspan="2"></td><td colspan="4"></td><td colspan="2"></td></tr></table>														EQUIPMENT		DESCRIPTION		EQUIPMENT		DESCRIPTION		LINK COLOR						SERVER / WORKSTATION ADVANTECH				ETHERNET SWITCH KYLAND				FIBER OPTIC PATCH CORD MULTIMODE						BAY CONTROL UNIT / COMMON IED IO SCHNEIDER ELECTRIC				PROTECTION RELAY SCHNEIDER ELECTRIC MICOM				UTP CAT-4 CABLE						ETHERNET SWITCH KYLAND								RS232/RS485 CABLE						ROUTER								COAXIAL CABLE						PROTECTION RELAY SCHNEIDER ELECTRIC MICOM								VGA, KEYBOARD, MOUSE CABLE						AUTOMATIC VOLTAGE REGULATOR A-EBERLE (REG-DA)														MODEM DCE (IG202T)														GATEWAY SCHNEIDER ELECTRIC SAITEL DP														ENERGY METER SCHNEIDER ELECTRIC (ION 8650)														MONITOR														KEYBOARD & MOUSE														SPEAKER														ANTENNE GPS														GPS TIME REFERENCE CLOCK HOPF 8030HEPTA														LASER PRINTER														ENGINEERING WORKSTATION														KVM EXTENDER												B	
EQUIPMENT		DESCRIPTION		EQUIPMENT		DESCRIPTION		LINK COLOR	
		SERVER / WORKSTATION ADVANTECH				ETHERNET SWITCH KYLAND				FIBER OPTIC PATCH CORD MULTIMODE	
		BAY CONTROL UNIT / COMMON IED IO SCHNEIDER ELECTRIC				PROTECTION RELAY SCHNEIDER ELECTRIC MICOM				UTP CAT-4 CABLE	
		ETHERNET SWITCH KYLAND								RS232/RS485 CABLE	
		ROUTER								COAXIAL CABLE	
		PROTECTION RELAY SCHNEIDER ELECTRIC MICOM								VGA, KEYBOARD, MOUSE CABLE	
		AUTOMATIC VOLTAGE REGULATOR A-EBERLE (REG-DA)	
		MODEM DCE (IG202T)	
		GATEWAY SCHNEIDER ELECTRIC SAITEL DP	
		ENERGY METER SCHNEIDER ELECTRIC (ION 8650)	
		MONITOR	
		KEYBOARD & MOUSE	
		SPEAKER	
		ANTENNE GPS	
		GPS TIME REFERENCE CLOCK HOPF 8030HEPTA	
		LASER PRINTER	
		ENGINEERING WORKSTATION	
		KVM EXTENDER	
C																C	
D																D	
E																E	
F		<table><tr><td rowspan="4">PT. ANTAM Tbk.</td><td colspan="2">Contractor</td><td colspan="2">: PT. HIGH VOLT TECHNOLOGY</td><td rowspan="4">PT. SCHNEIDER INDONESIA</td><td colspan="4">SUBSTATION AUTOMATION SYSTEM ARCHITECTURE DIAGRAM LEGEND GENERAL OVERVIEW</td><td>Format</td><td>Scale</td><td>Drawn By</td><td>FSR</td><td>Date</td><td>Revision</td></tr><tr><td colspan="2">Project Name</td><td colspan="2">: GI 150KV ANTAM POMALAA - SAS & CRP</td><td>A3</td><td>NTS</td><td>Checked By</td><td>HK</td><td>9/25/2023</td><td>A</td></tr><tr><td colspan="2">Customer Order No</td><td colspan="2">: 200/HVT-SCHNEIDERINDONESIA/ PO/VIII/2023 R1 - dated: 2023-08-14</td><td></td><td></td><td>Appr. By</td><td>TNN</td><td>Sheet</td><td>Next Sheet</td></tr><tr><td colspan="4"></td><td colspan="4">Drawing No. : E2010-96317-BD-01-SAD</td><td colspan="2">003</td><td colspan="2">004</td></tr></table>														 PT. ANTAM Tbk.	Contractor		: PT. HIGH VOLT TECHNOLOGY		 PT. SCHNEIDER INDONESIA	SUBSTATION AUTOMATION SYSTEM ARCHITECTURE DIAGRAM LEGEND GENERAL OVERVIEW				Format	Scale	Drawn By	FSR	Date	Revision	Project Name		: GI 150KV ANTAM POMALAA - SAS & CRP		A3	NTS	Checked By	HK	9/25/2023	A	Customer Order No		: 200/HVT-SCHNEIDERINDONESIA/ PO/VIII/2023 R1 - dated: 2023-08-14				Appr. By	TNN	Sheet	Next Sheet					Drawing No. : E2010-96317-BD-01-SAD				003		004		F	
 PT. ANTAM Tbk.	Contractor		: PT. HIGH VOLT TECHNOLOGY		 PT. SCHNEIDER INDONESIA	SUBSTATION AUTOMATION SYSTEM ARCHITECTURE DIAGRAM LEGEND GENERAL OVERVIEW				Format	Scale	Drawn By	FSR	Date	Revision	
	Project Name		: GI 150KV ANTAM POMALAA - SAS & CRP			A3	NTS	Checked By	HK	9/25/2023	A	
	Customer Order No		: 200/HVT-SCHNEIDERINDONESIA/ PO/VIII/2023 R1 - dated: 2023-08-14					Appr. By	TNN	Sheet	Next Sheet	
						Drawing No. : E2010-96317-BD-01-SAD				003		004	
1		2		3		4		5		6		7		8	

Substation Automation Architecture for 150kV ANTAM POMALAA

Legend	
	Fiber Optic Patch Cord
	Multimode
	UTP CAT-4 Cable
	RS232/RS485 Cable
	Coaxial Cable
	VGA, Keyboard, Mouse Cables

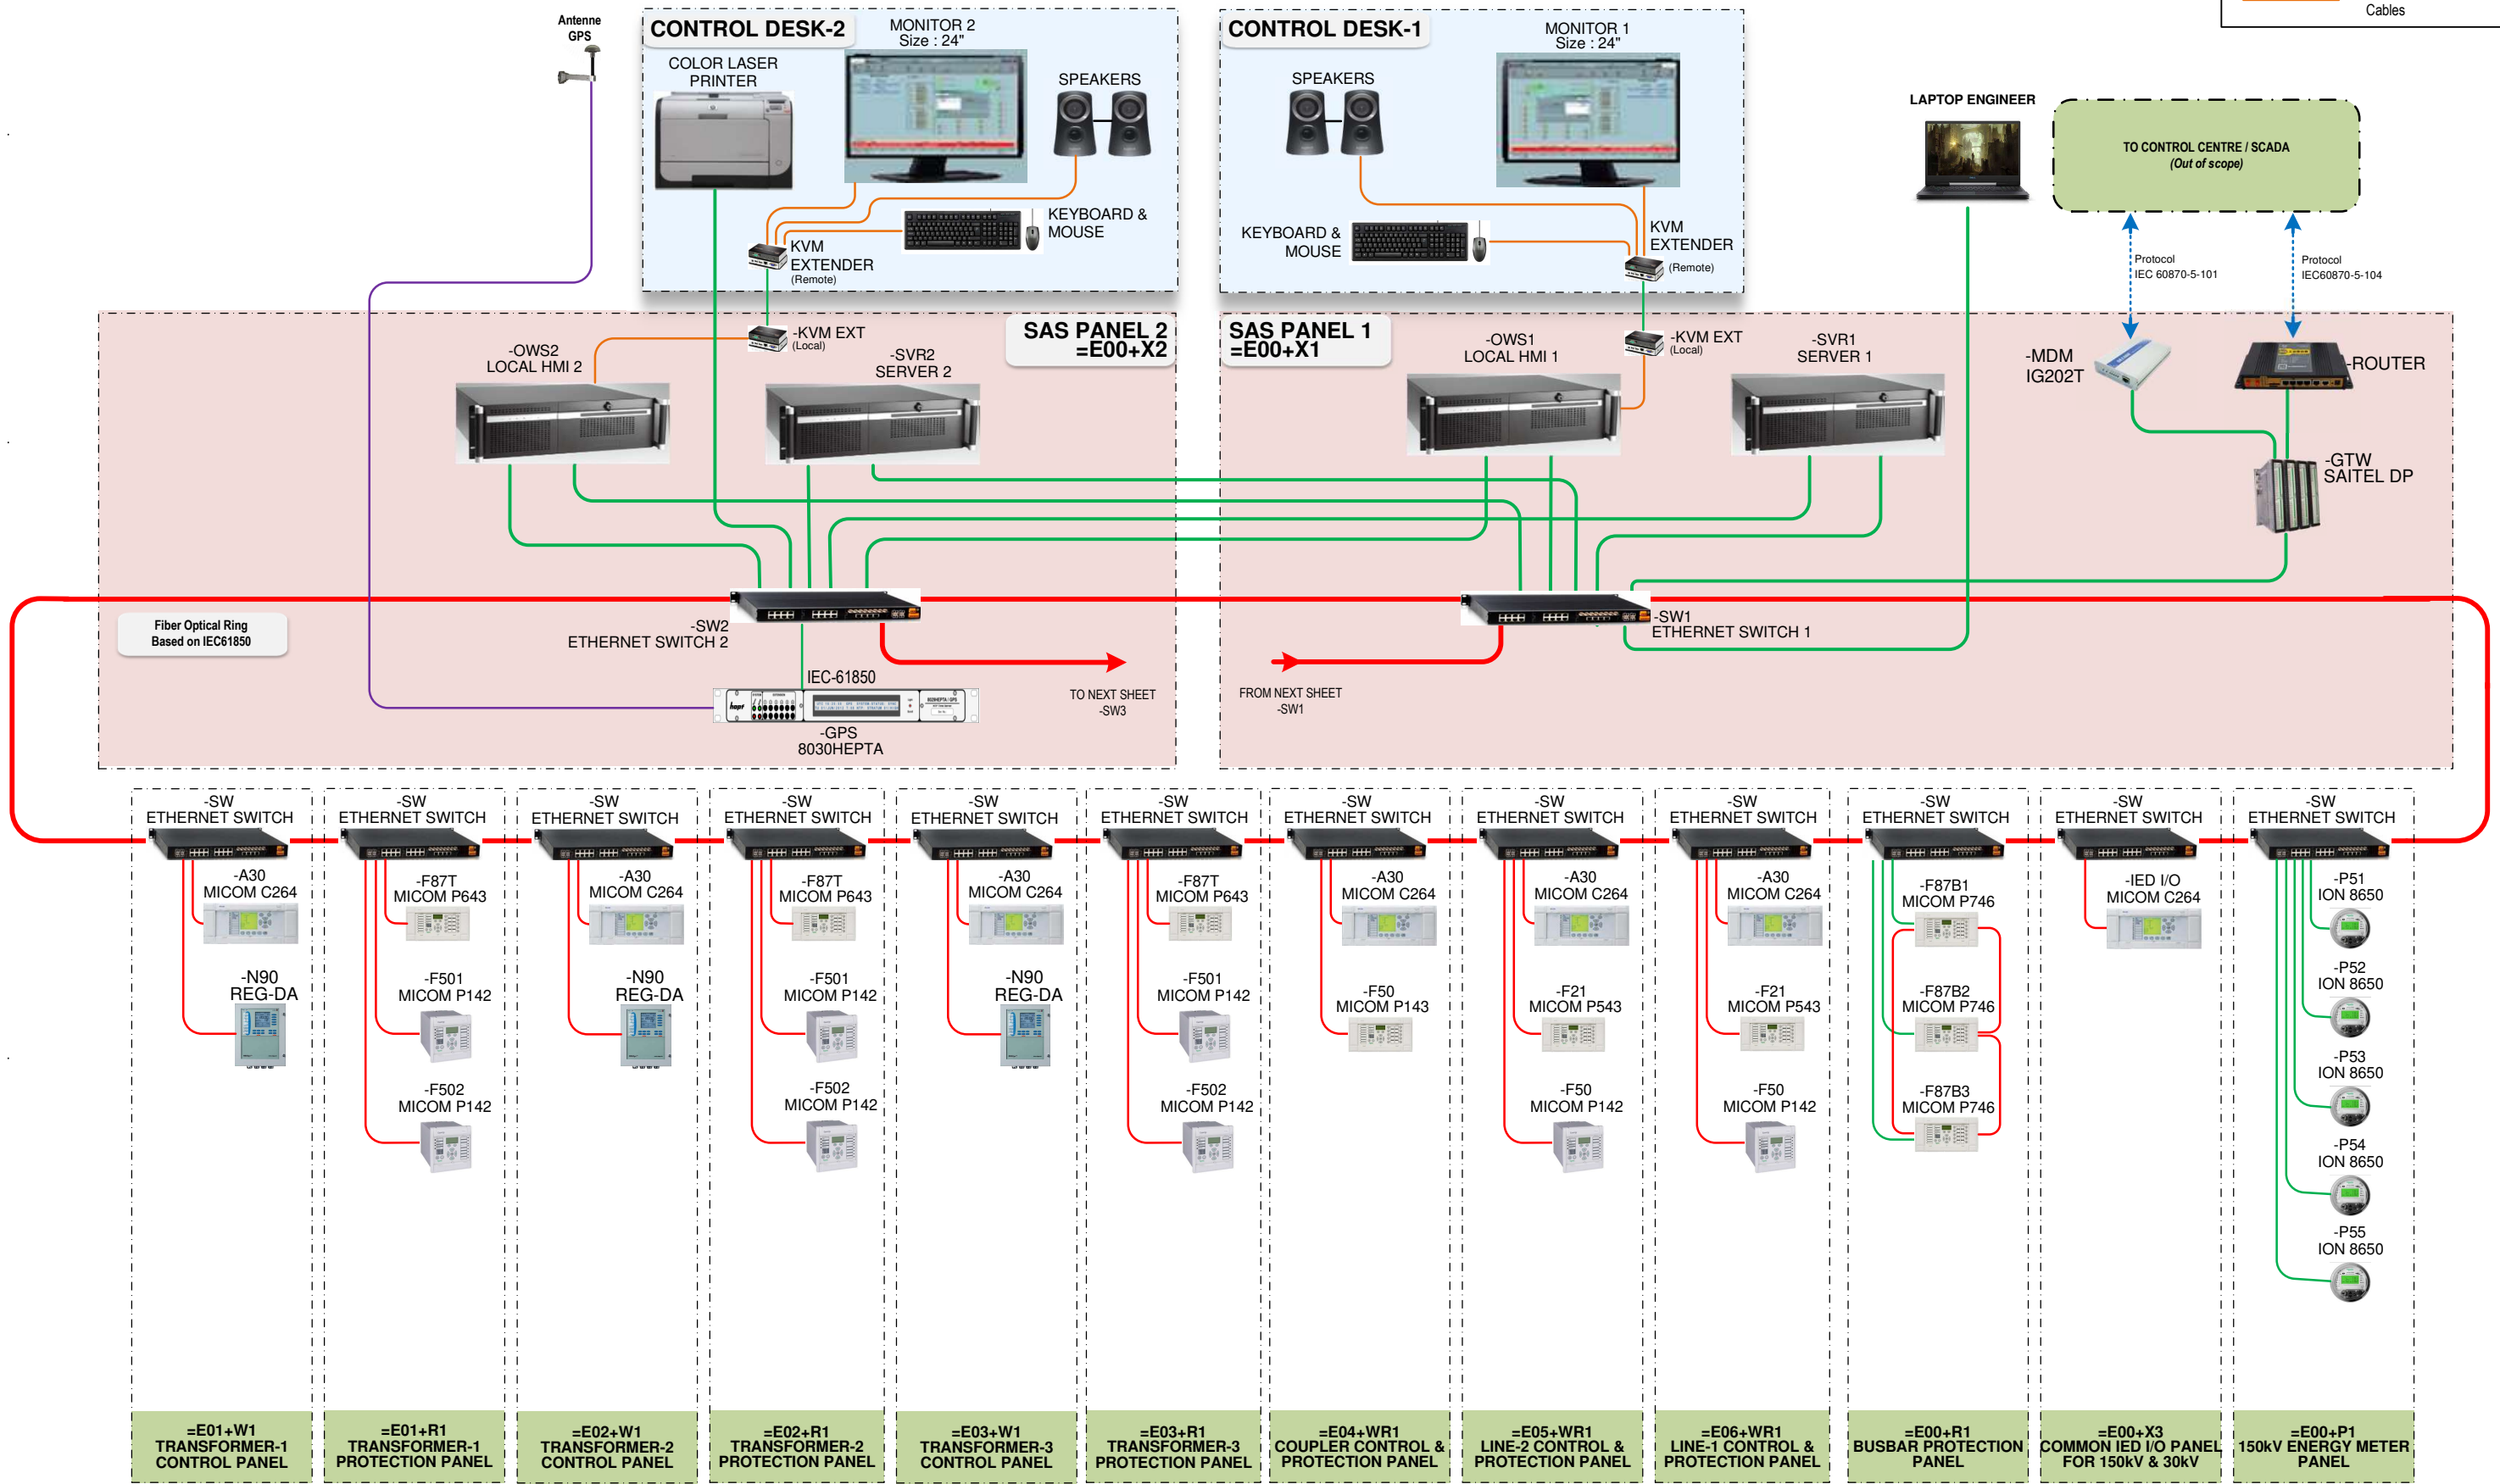

Substation Automation Architecture for 150kV ANTAM POMALAA

Legend

Fiber Optic Patch Cord

Multimode

UTP CAT-4 Cable

RS232/RS485 Cable

Coaxial Cable

VGA, Keyboard, Mouse Cables

